

# RFR

4, Rue Maillard  
75011 PARIS  
Tél. (1) 40 09 21 12  
Télécopie (1) 40 09 83 38

## T E L E C O P I E

Destinée à : MUMBERT CAMERLO

Date : 11/05

N° de télécopie  
du destinataire : 67 73 30 65

Nbre de pages : 11  
(incluant celle-ci)

Envoi provenant de : NICOLAS

Copies :

Affaire : THEATRE DE LA PLEINE LUNE

Objet :

### M E S S A G E


VOICI LES TELECOPIES QUE J'AI  
ENVOYÉES CE MATIN.

- JE N'AI ENVOYÉ AU CINTREUR  
QUE DE QUOI CINTREUR 16 RAILS  
CAR LA PARABOLE N° 9

CHEVAUCHE PRESQUE COMPLETEMENT  
LA PARABOLE N° 8.

- POUR LES EXTREMITÉS DU PORTIQUE  
A GAUCHE ET A DROITE, NOUS RISQUONS  
DE NE PAS POUVOIR LE MONTER  
TOTALLEMENT NOTAMMENT A DROITE : LES  
MONTEURS S'ADAPTERONS EN FONCTION  
DU TERRAIN.

MEILLEURES SALUTATIONS  
NICOLAS.

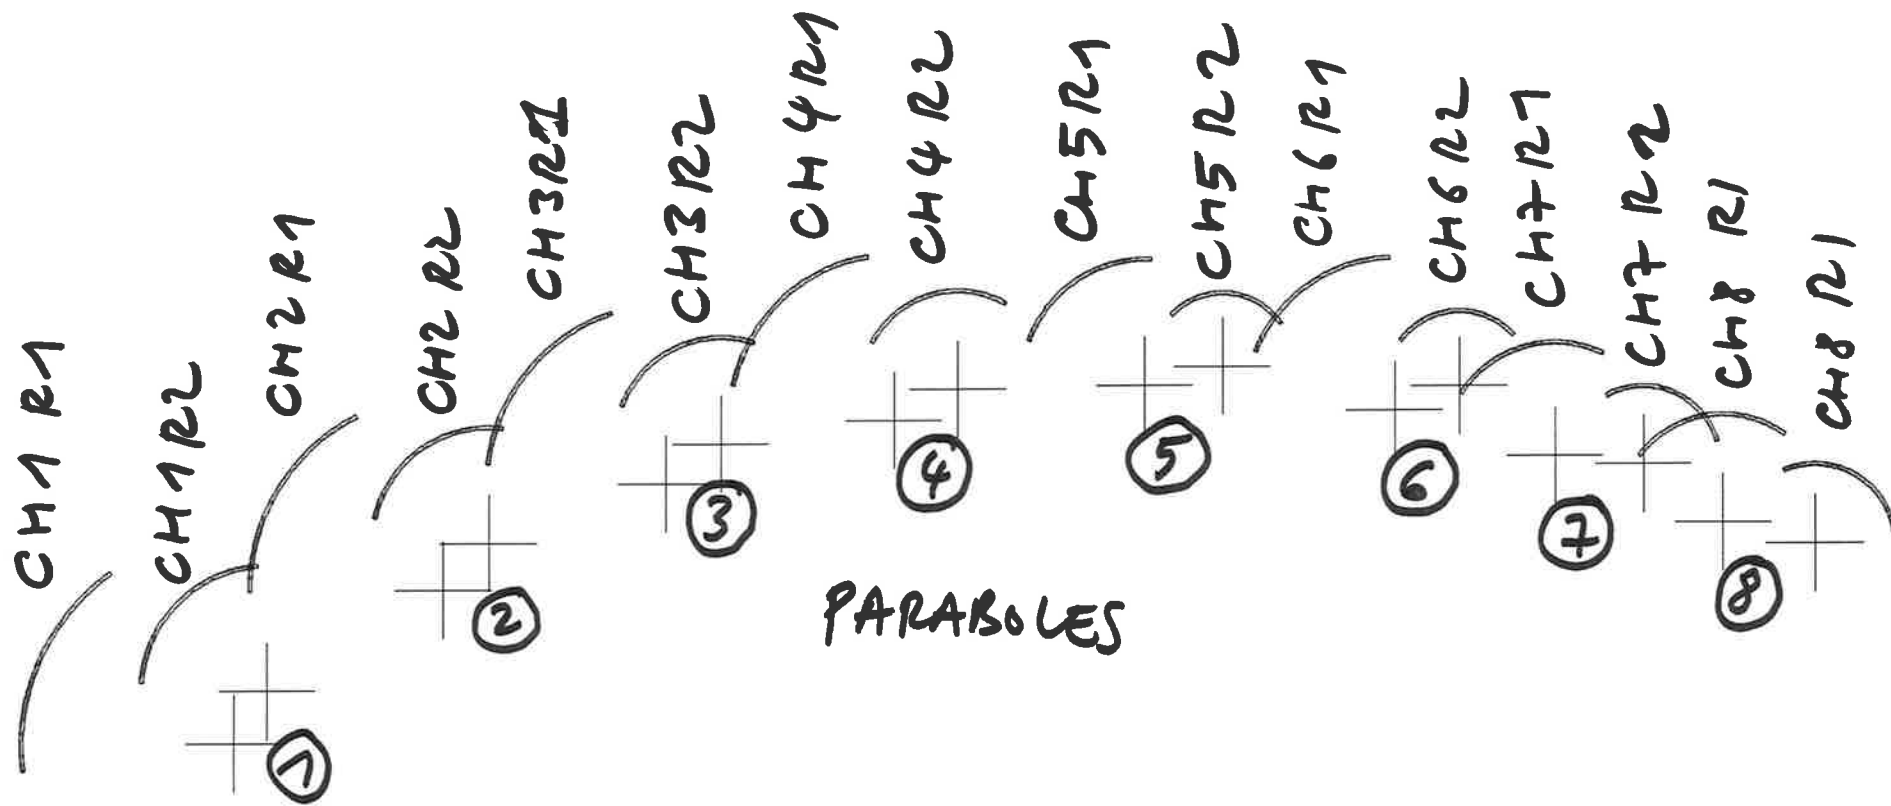

# RFR

4, Rue Maillard  
75011 PARIS  
Tél. (1) 40 09 21 12  
Télécopie (1) 40 09 83 38

## TELECOPIE

Destinée à : ENTREE POSE  
M. CASADO  
N° de télécopie  
du destinataire : 61 70 41 70

Date : 11/05

Nbre de pages : 3  
(incluant celle-ci)

Envoi provenant de : N. PROUVÉ

Copies : M. CAMERLO

Affaire : THEATRE DE LA PLEINE LUNE

Objet : PORTIQUE


### MESSAGE

VOICI LA DEFINITION DU PORTIQUE  
EN PLAN DONT NOUS VENONS  
DE PARLER AU TELEPHONE.


- LE PORTIQUE DEURA ETRE MONTE POUR  
VENDREDI 15 MAI DANS LA JOURNEE.
- LA COUPE DU PORTIQUE TELLE QUE  
VOUS ME L'AVEZ ENVOYEE DANS  
VOTRE FAX DU 29/04 RESTE  
VALABLE.

MEILLEURES SALUTATIONS

NICOLAS PROUVÉ.

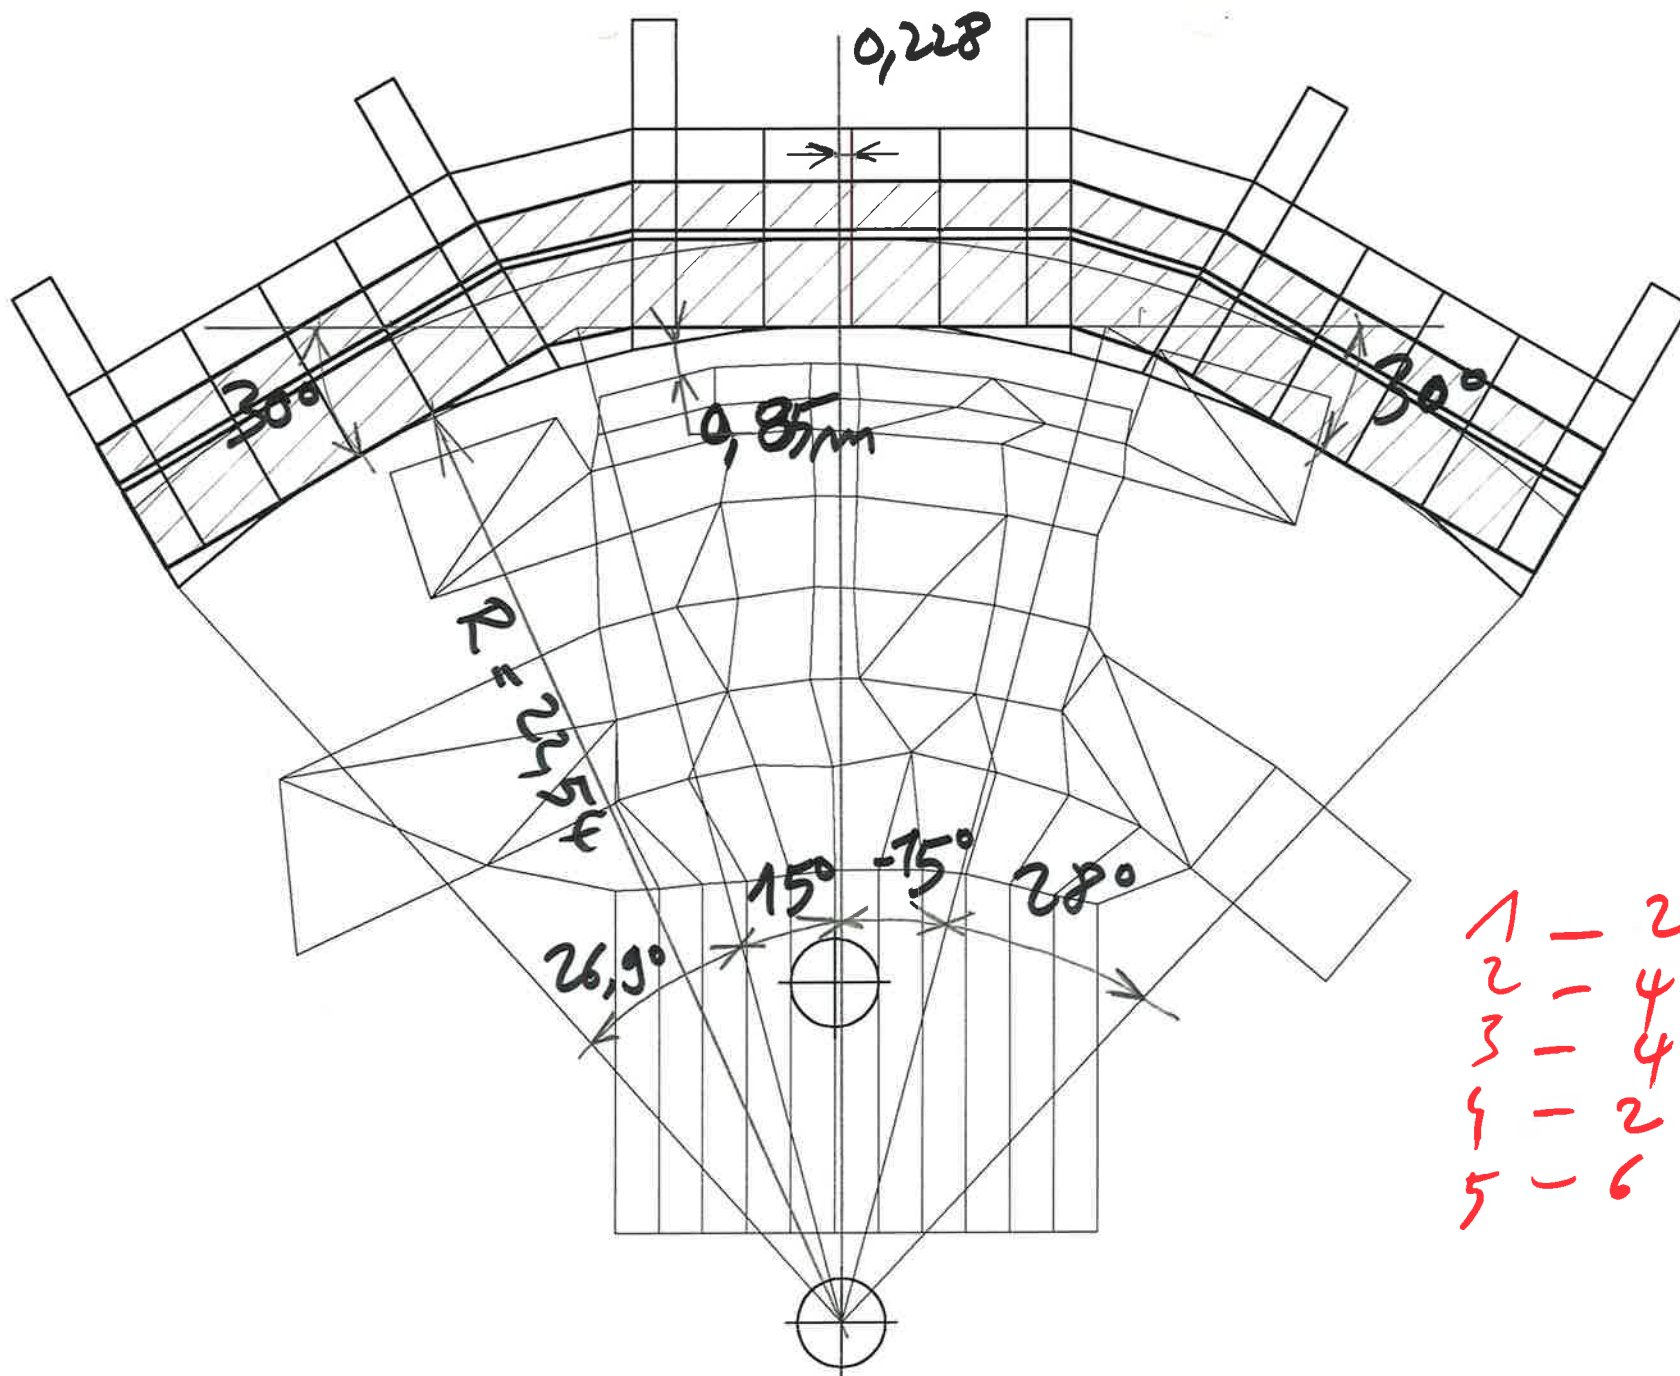

1 - 2  
 2 - 4  
 3 - 4  
 4 - 2  
 5 - 6

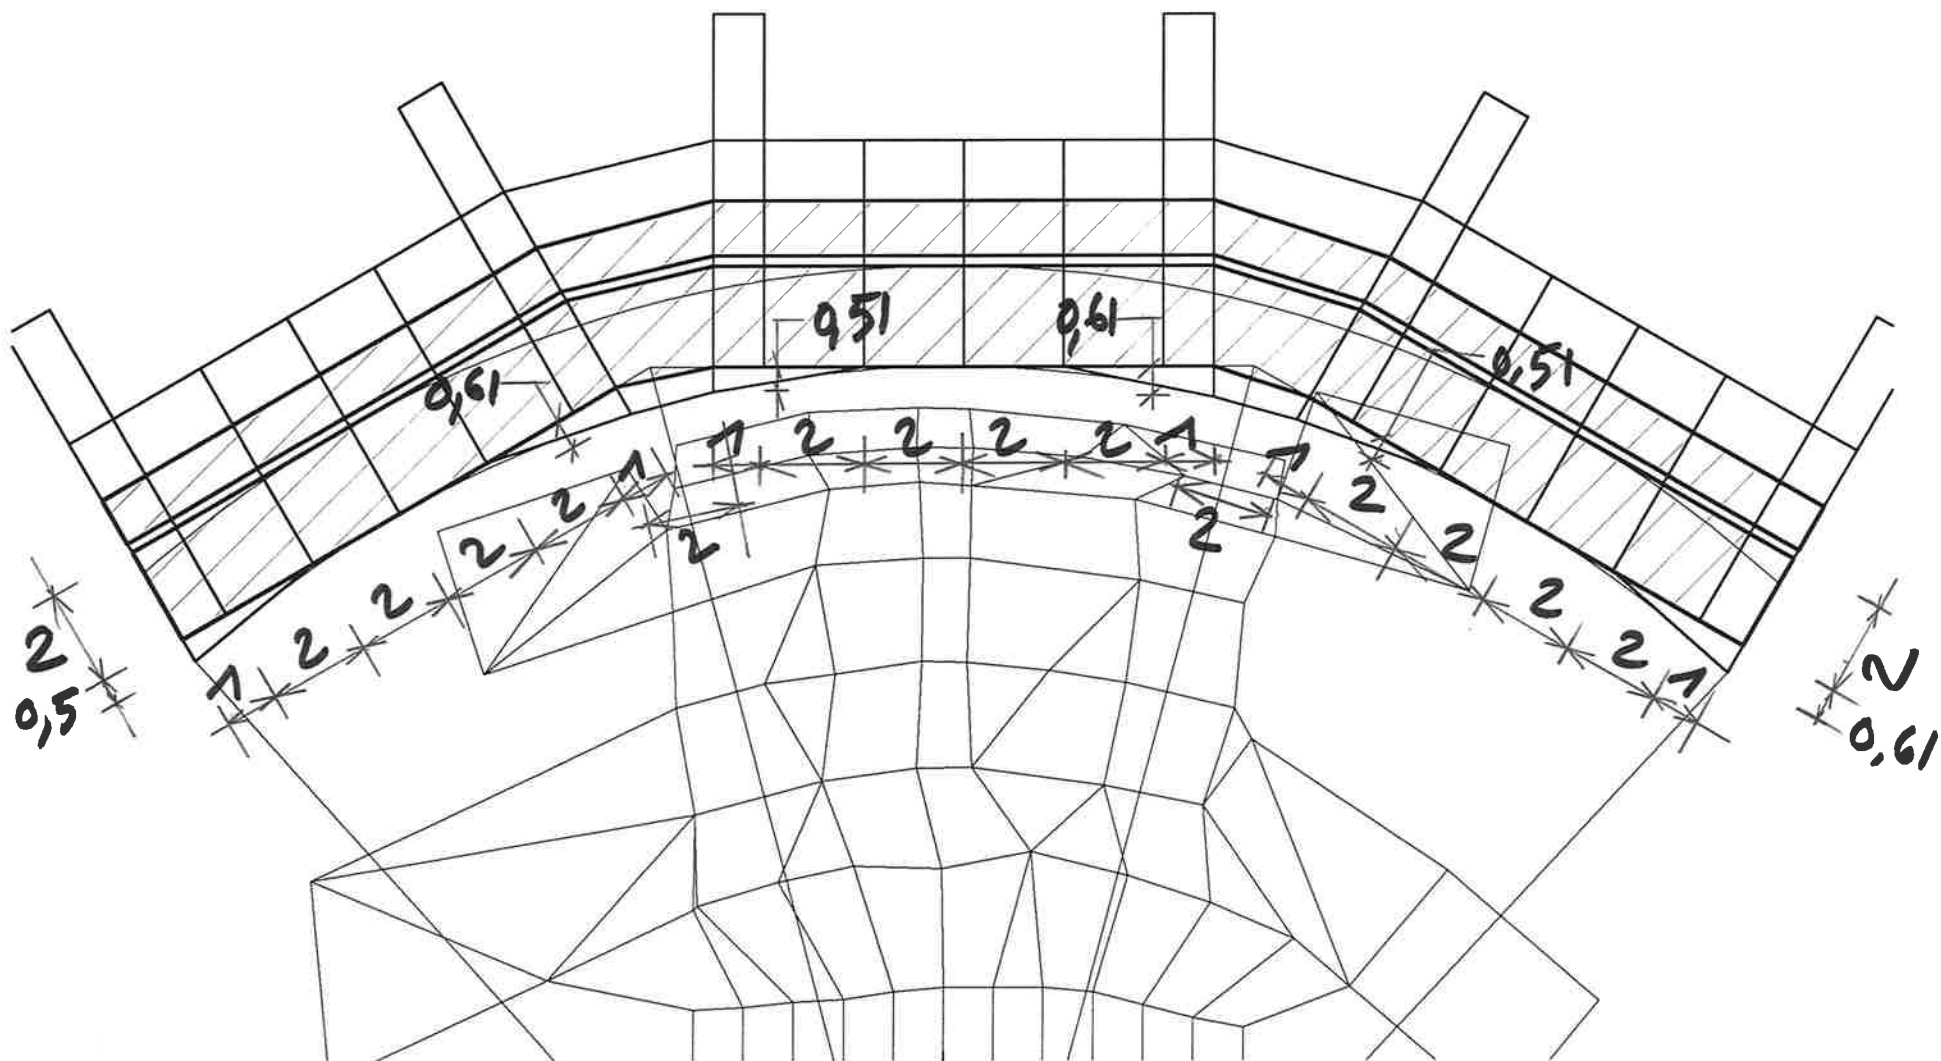

# RFR

4, Rue Maillard  
75011 PARIS  
Tél. (1) 40 09 21 12  
Télécopie (1) 40 09 83 38

## T E L E C O P I E

Destinée à : ANDREW SEDGWICK

Date : 11/05

N° de télécopie  
du destinataire : 1944 71 465 3743

Nbre de pages : 4  
(incluant celle-ci)

Envoi provenant de : NICOLAS

Copies : HUMBERT.

Affaire : THEATRE OF THE FULL MOON

Objet :

## M E S S A G E


PLEASE FIND ENCLOSED, THE  
GEOMETRIE OF THE HIGH MIRRORS'  
SUPPORT.



THESE MIRRORS ARE FIXED AND  
ARE ADJUSTED FOR 1am.

THE SIZE OF MIRRORS PANELS  
ARE 0,72m x 0,72m

REGARDS

NICOLAS.

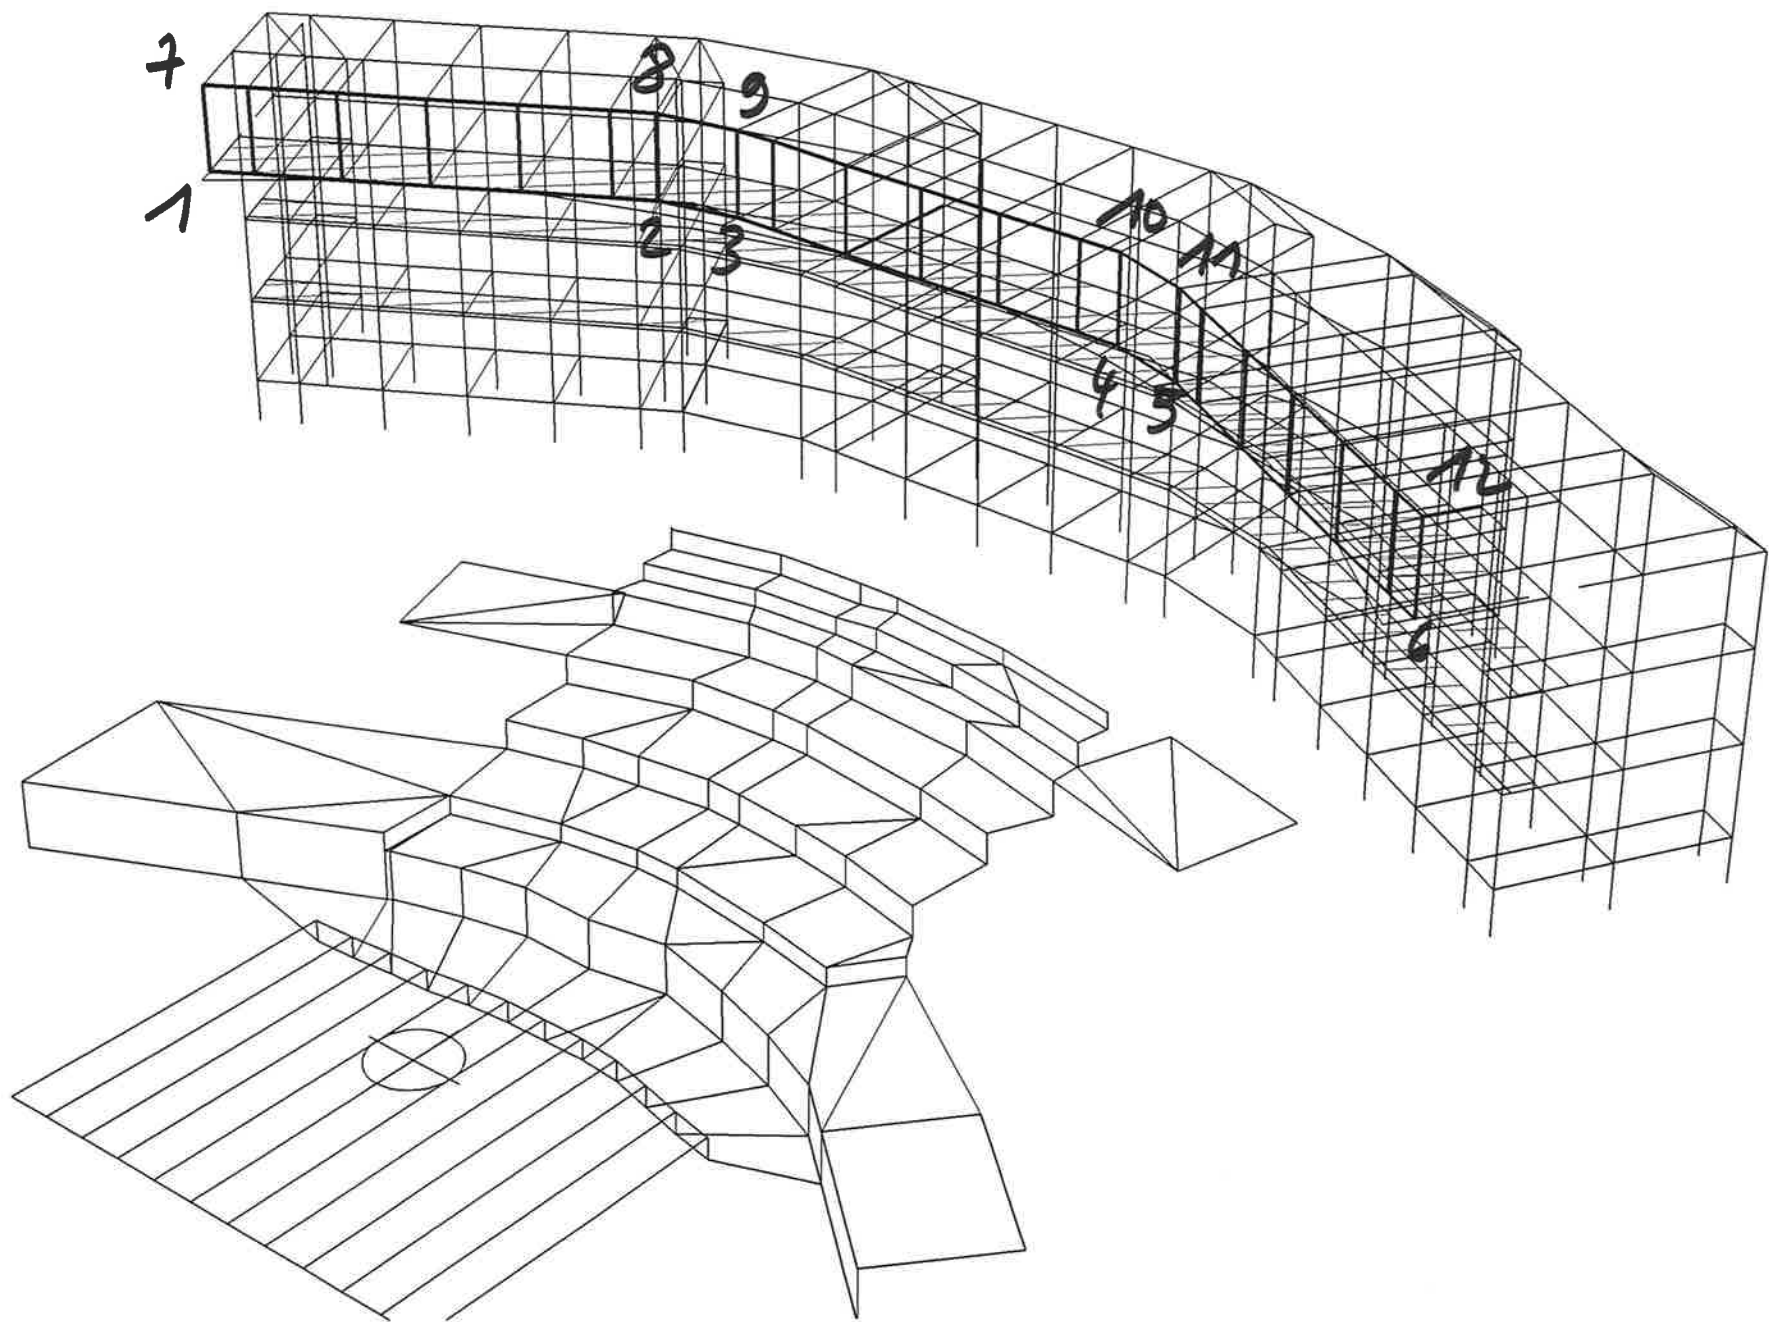

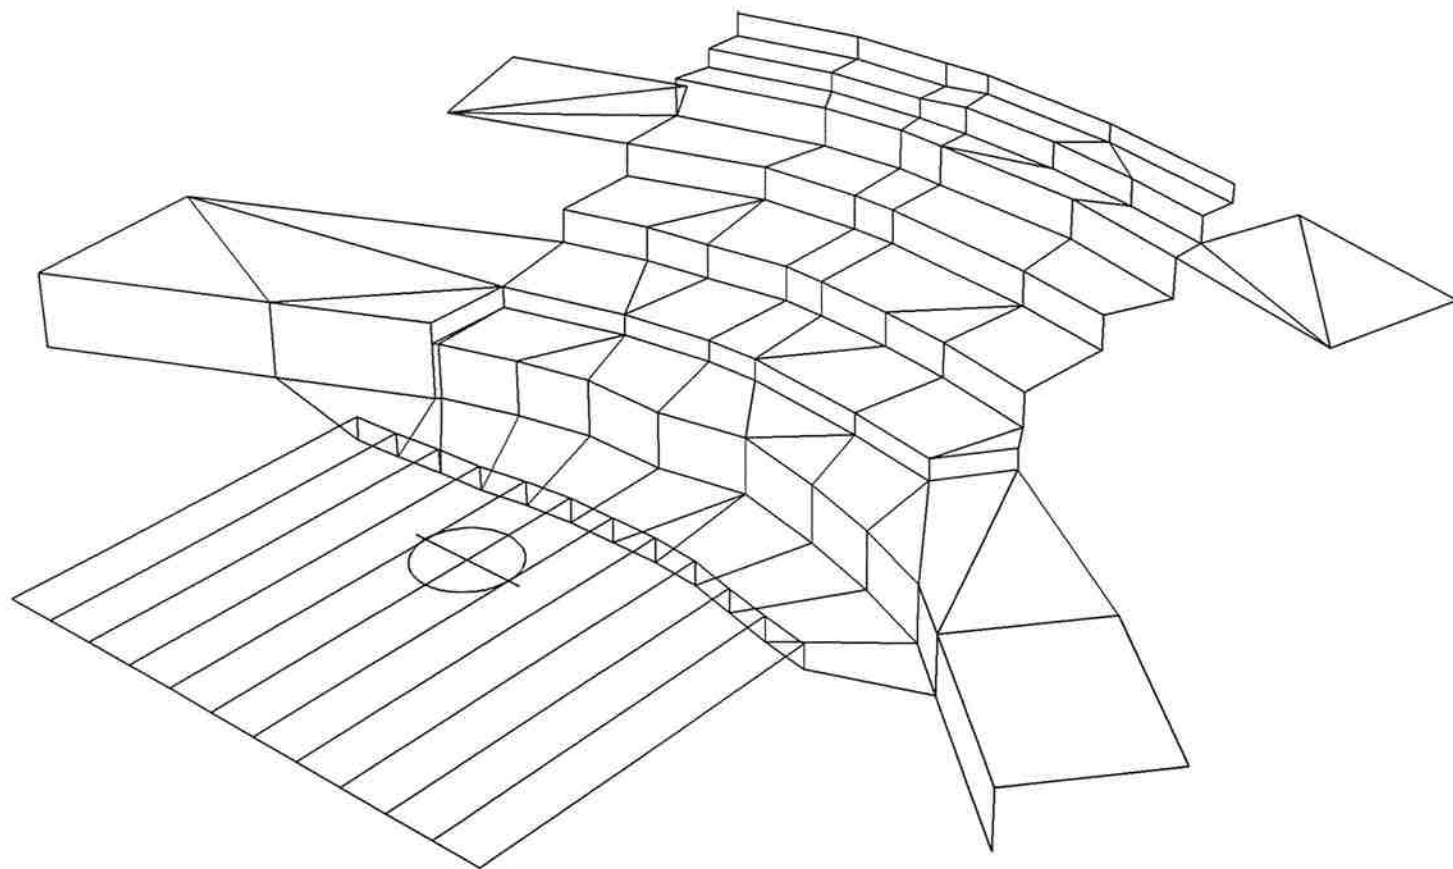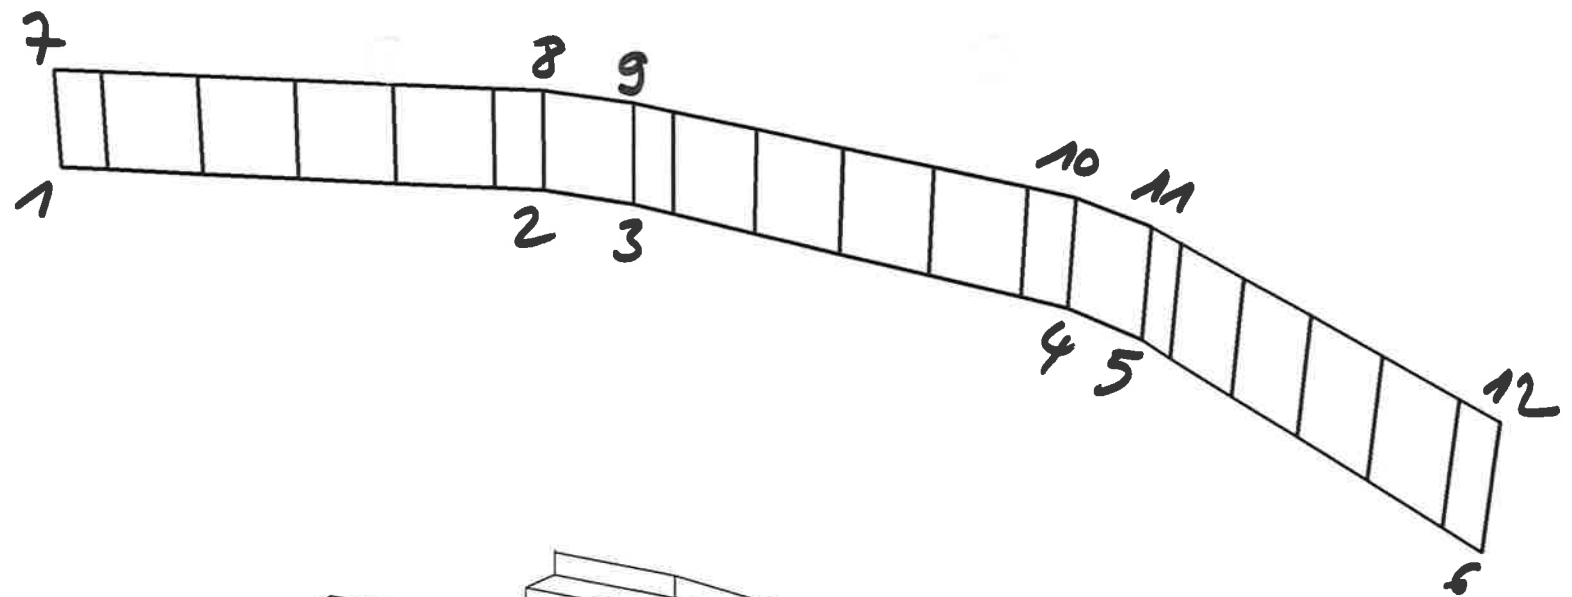



# COORDINATES:

| POINTS | X      | Y     | Z     |
|--------|--------|-------|-------|
| 1      | -15,23 | 9,47  | 11,88 |
| 2      | -6,57  | 14,46 | 11,88 |
| 3      | -4,61  | 14,87 | 11,88 |
| 4      | 5,39   | 14,87 | 11,88 |
| 5      | 7,29   | 14,24 | 11,88 |
| 6      | 15,95  | 9,24  | 11,88 |
| 7      | -15,23 | 9,47  | 13,32 |
| 8      | -6,57  | 14,46 | 13,32 |
| 9      | -4,61  | 14,87 | 13,32 |
| 10     | 5,39   | 14,87 | 13,32 |
| 11     | 7,29   | 14,24 | 13,32 |
| 12     | 15,95  | 9,24  | 13,32 |